


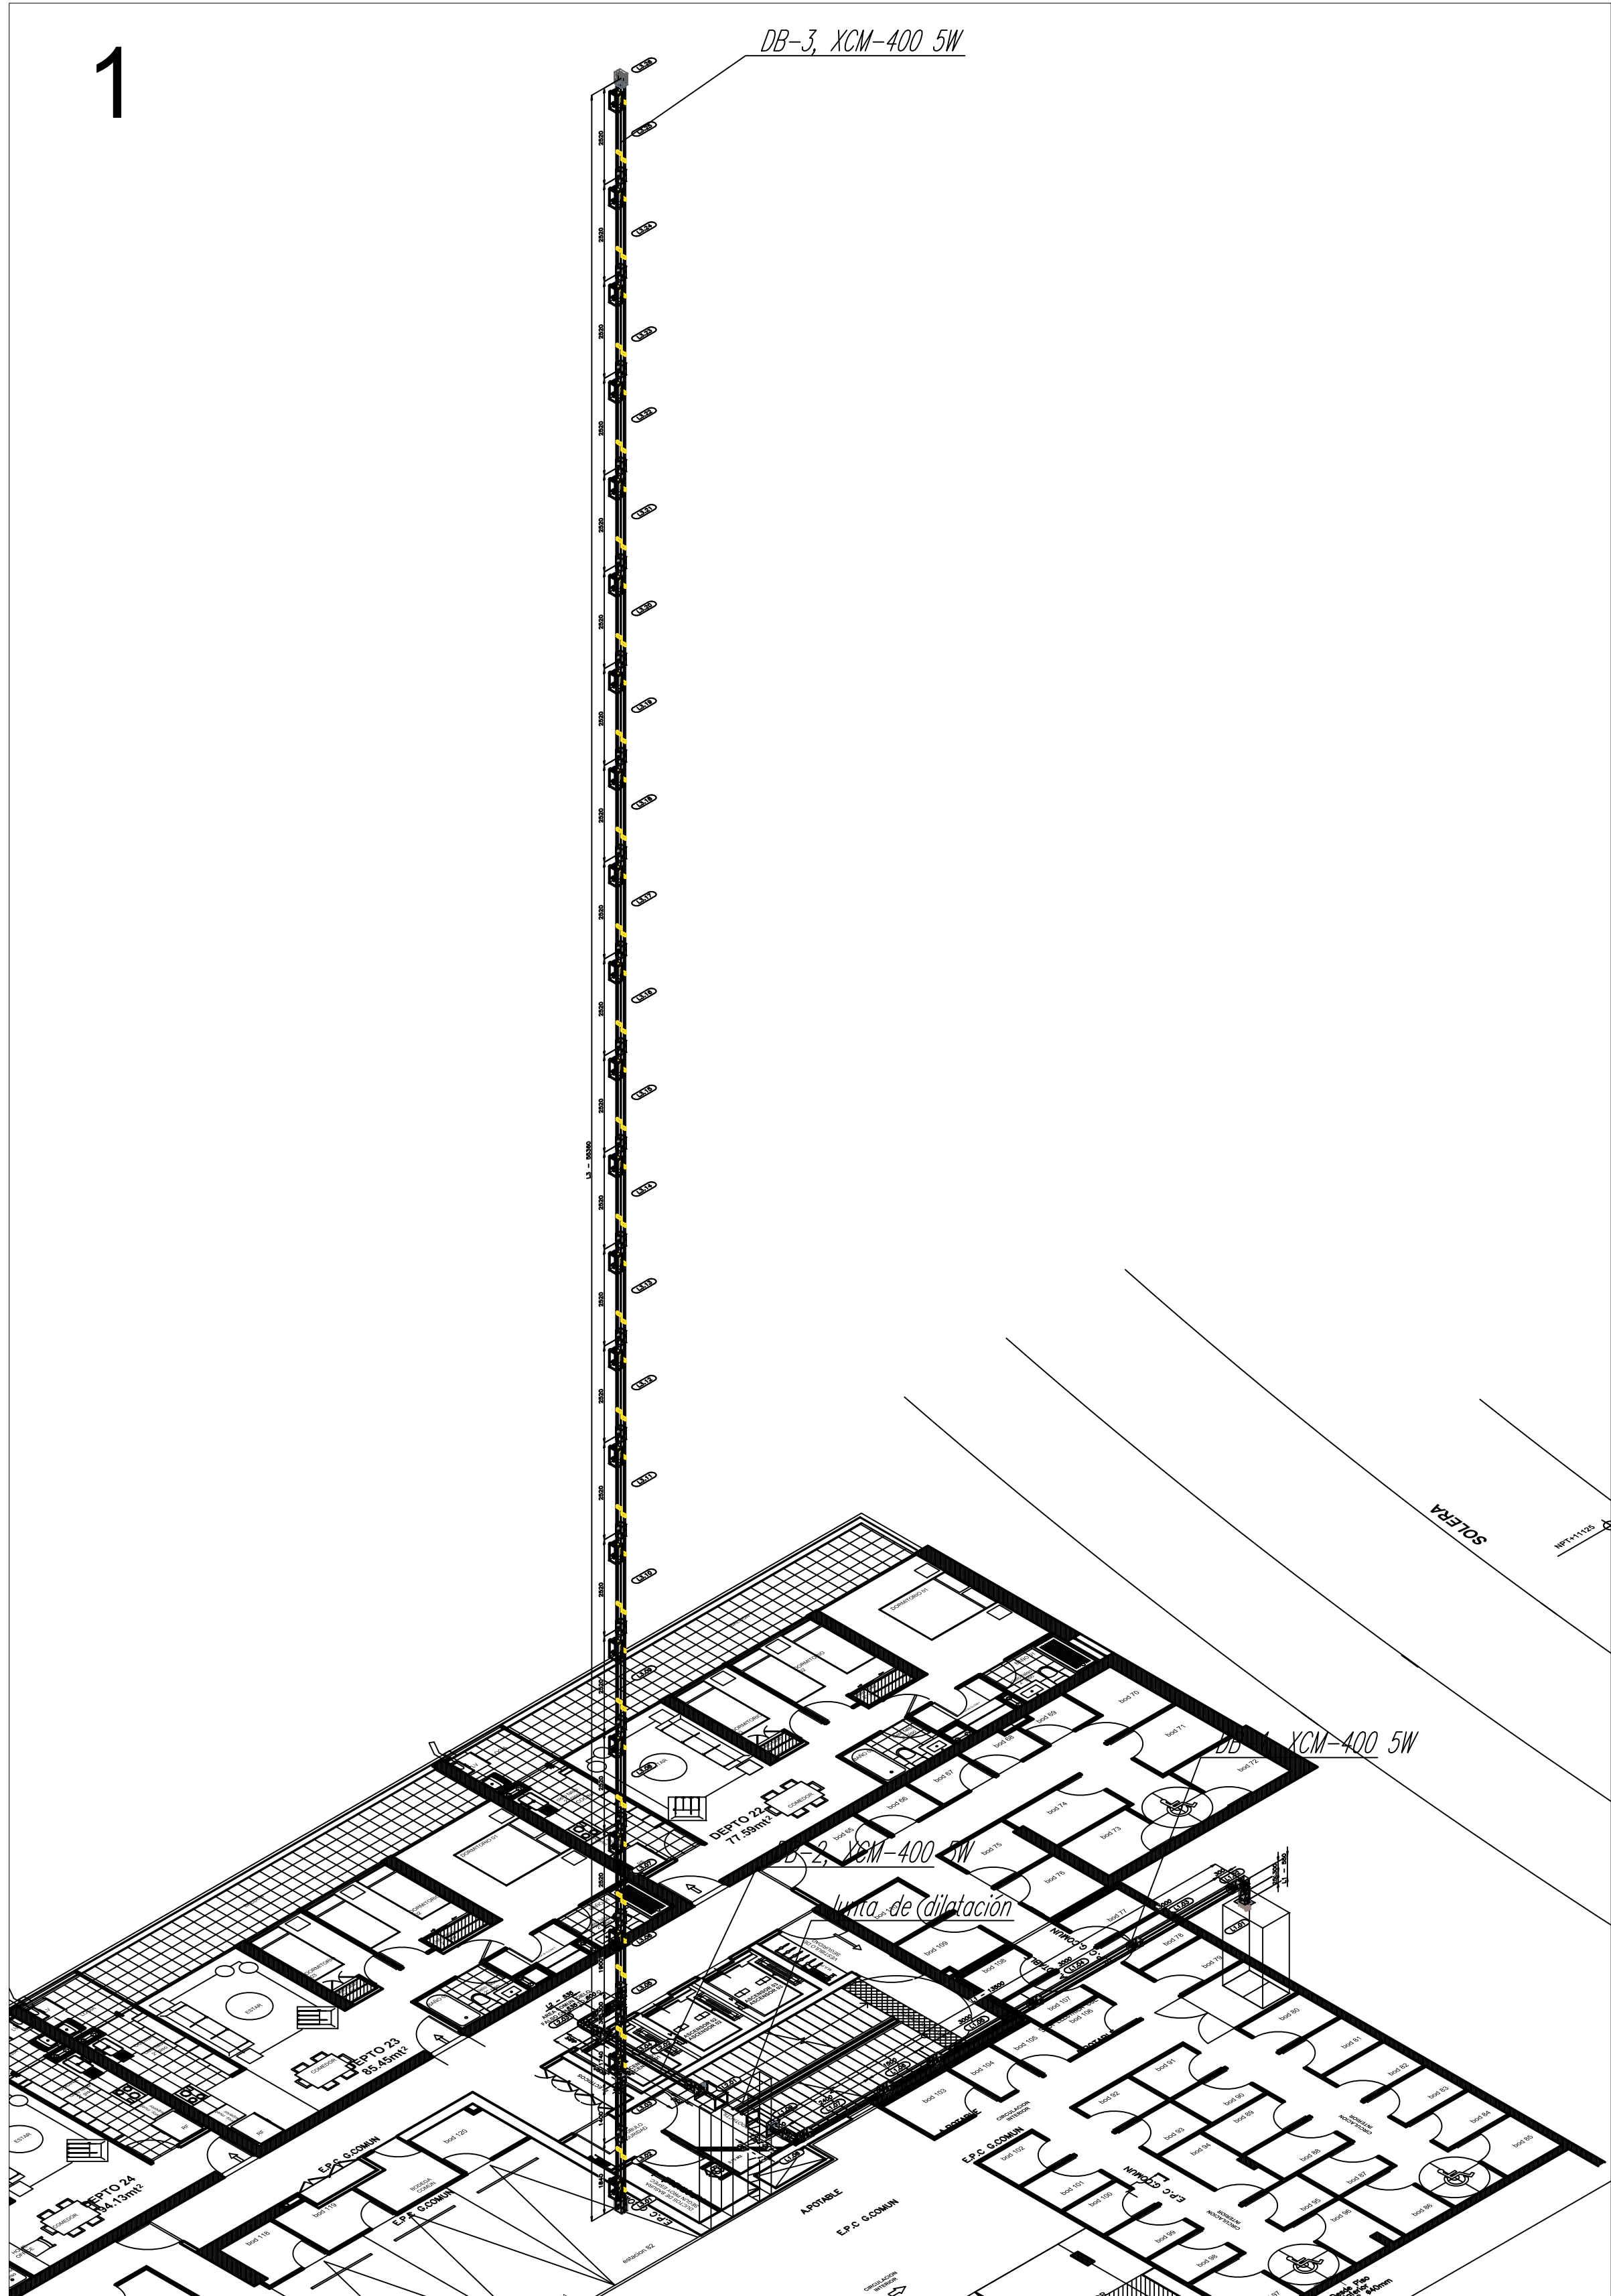


Vista isométrica estudio ducto barra.

número de línea
número de pieza

L2.03

NOMENCLATURA DE TAGS

B	1.04.2026	PLANO PARA APROBACION DEL CLIENTE	M. C.	J. H.	
A	26.03.2026	PLANO PARA APROBACION DEL CLIENTE	M. C.	J. H.	
Rev	Fecha	Descripción	Dib.	Apr.	

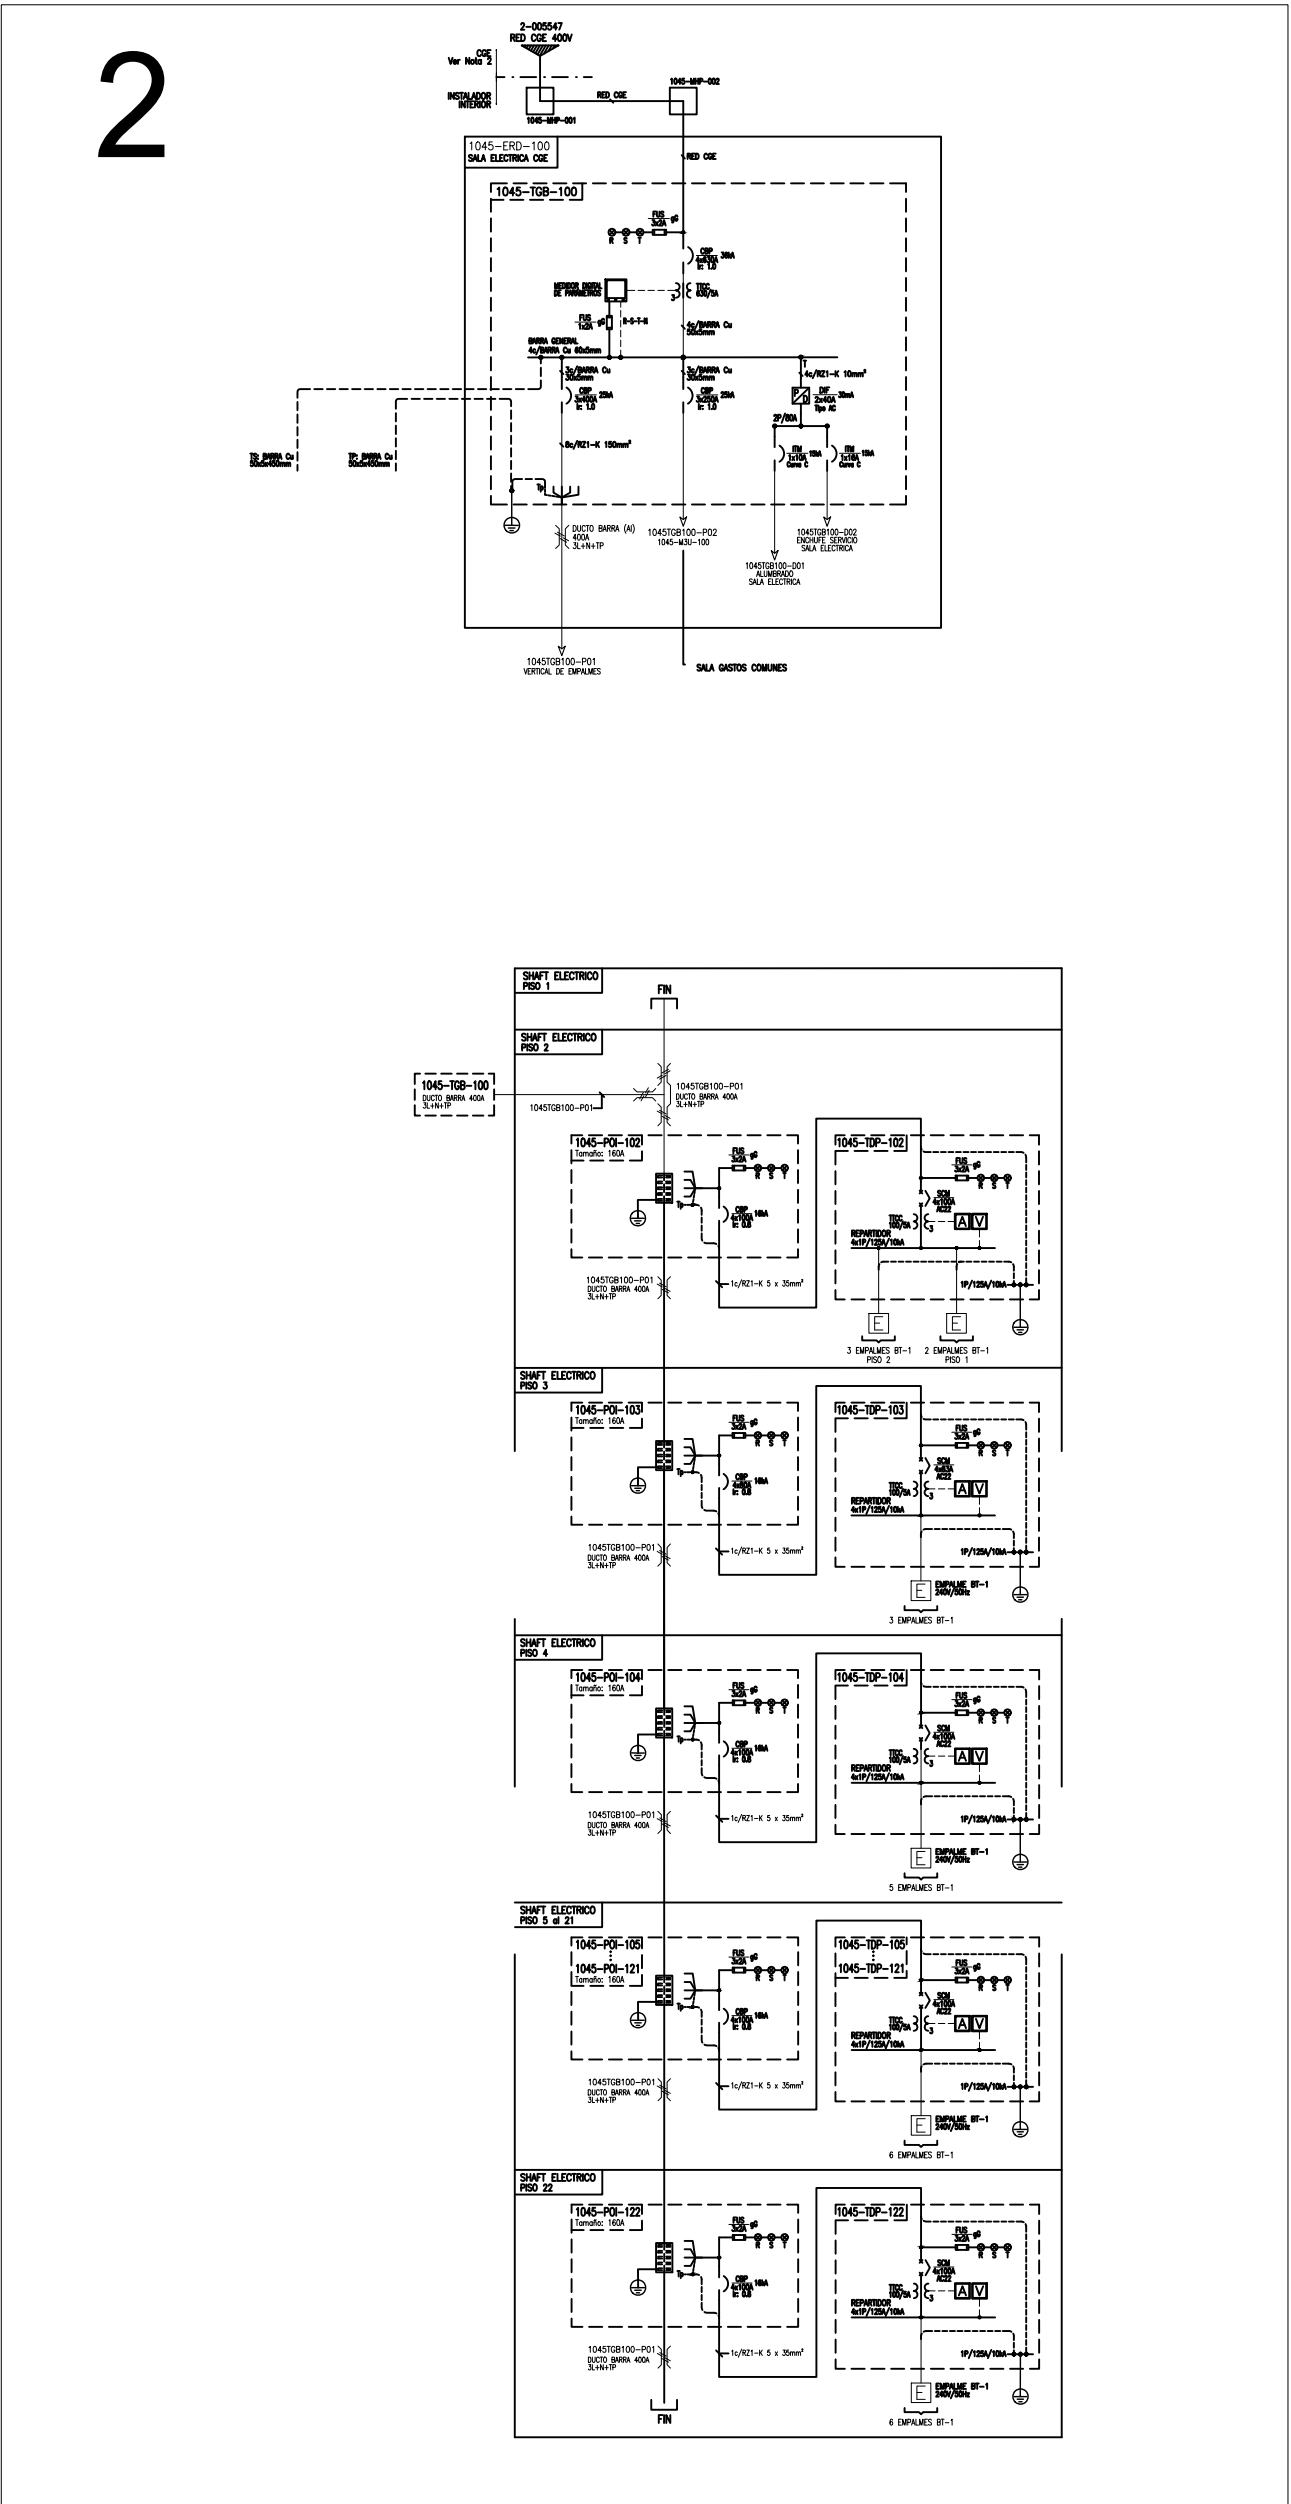

Extracto diagrama unilineal, proyecto eléctrico.

- NOTAS:
- Modulación hecha con datos aportados por el cliente y asistencia a obra el 10-3-26.
 - El cliente debe revisar cuidadosamente esta propuesta para dar su aprobación.
 - Se consideran ductos con barras de Aluminio, compacto y neutro al 100%.
 - Medidas de tableros h= 2100 x 1200 x 800, posición según proyecto eléctrico.
 - Avance horizontal a coordinar con avance de bandejas y otros servicios.
 - Profundidad libre fondo shaft mínimo 650mm hasta la puerta de cierre o muro, ver detalle.
 - Suministro de plug in aptos DPX.
 - Pasadas de muros y lozas por obra, inclusive sellos de todo tipo.
 - Los cables y terminales de interconexiones no son parte de esta oferta.
 - Abrazaderas fijas cada 1500mm max., con resortes según calibre ducto.
 - La soportación en vertical debe estar apoyada sobre concreto, de lo contrario es responsabilidad del cliente llevar a cálculo el sistema antes de instalar.
 - Si el proyecto considera arriba interno en la parte superior del tablero, este debe disponer de un espacio libre mínimo de 400mm hasta barras o protección.
 - Estudio a ser confirmado por mandante y verificado en terreno. Cambios posteriores a la cotización podrían generar diferencias en el valor final.
 - Niveles referenciales y en mm.
 - LAS COTAS PREVALECEAN SOBRE EL DIBUJO.
 - Encapsulado IP-55.
 - Clase aislamiento, 1000V.
 - Perno dinamométrico en la unión, autocalibrado, 85Nm de apriete.

			Proyecto: MODULACION DUCTO BARRA EDIFICIO SAN PETERSBURGO VISTAS GENERALES.		
Fecha: 01-04-2026	Revisó: J. Henriquez.	Proyectó: M. Campos.	Ref. Legrand: REQ-13XXX-26	archivo: 2603-604	Revisión: B
Escala: S/E	Formato: A1	Aprobó: L. Garcia.	Cliente: Guzmán y Larrain.		Lámina 1